
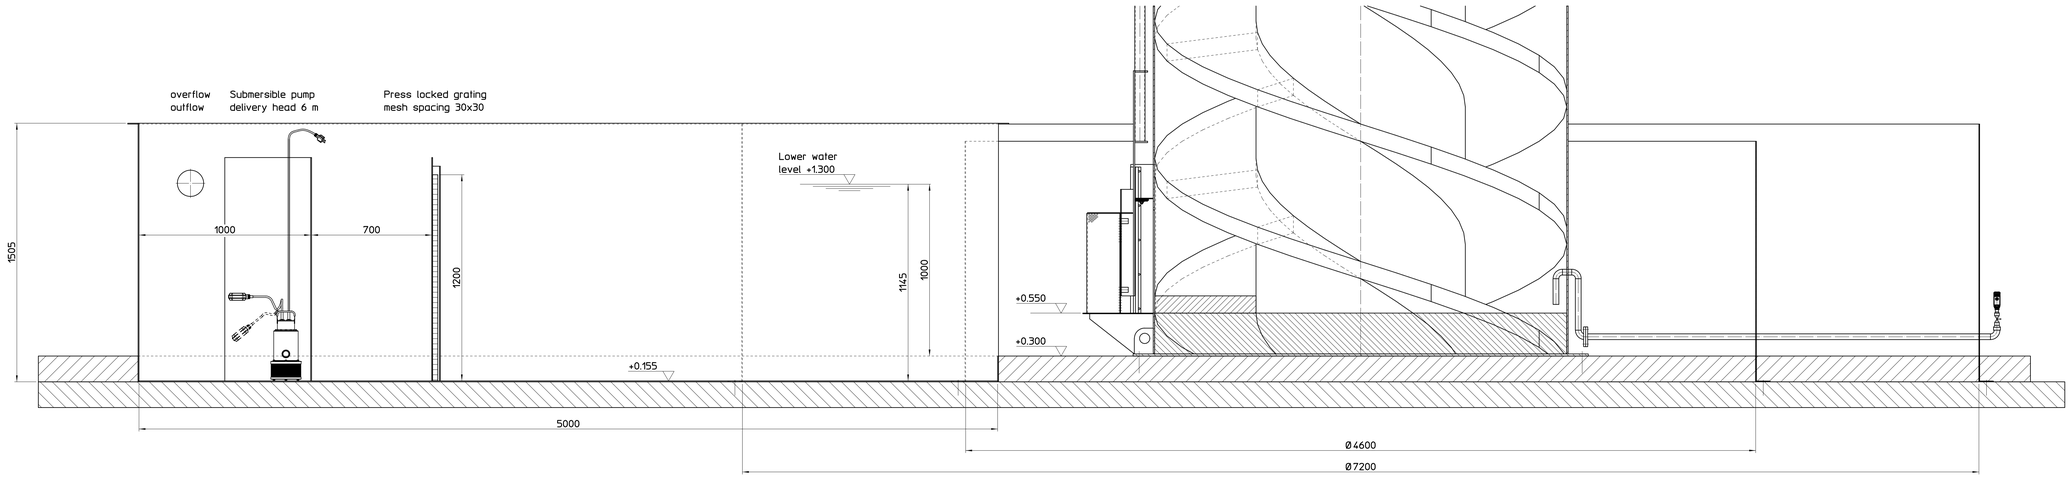


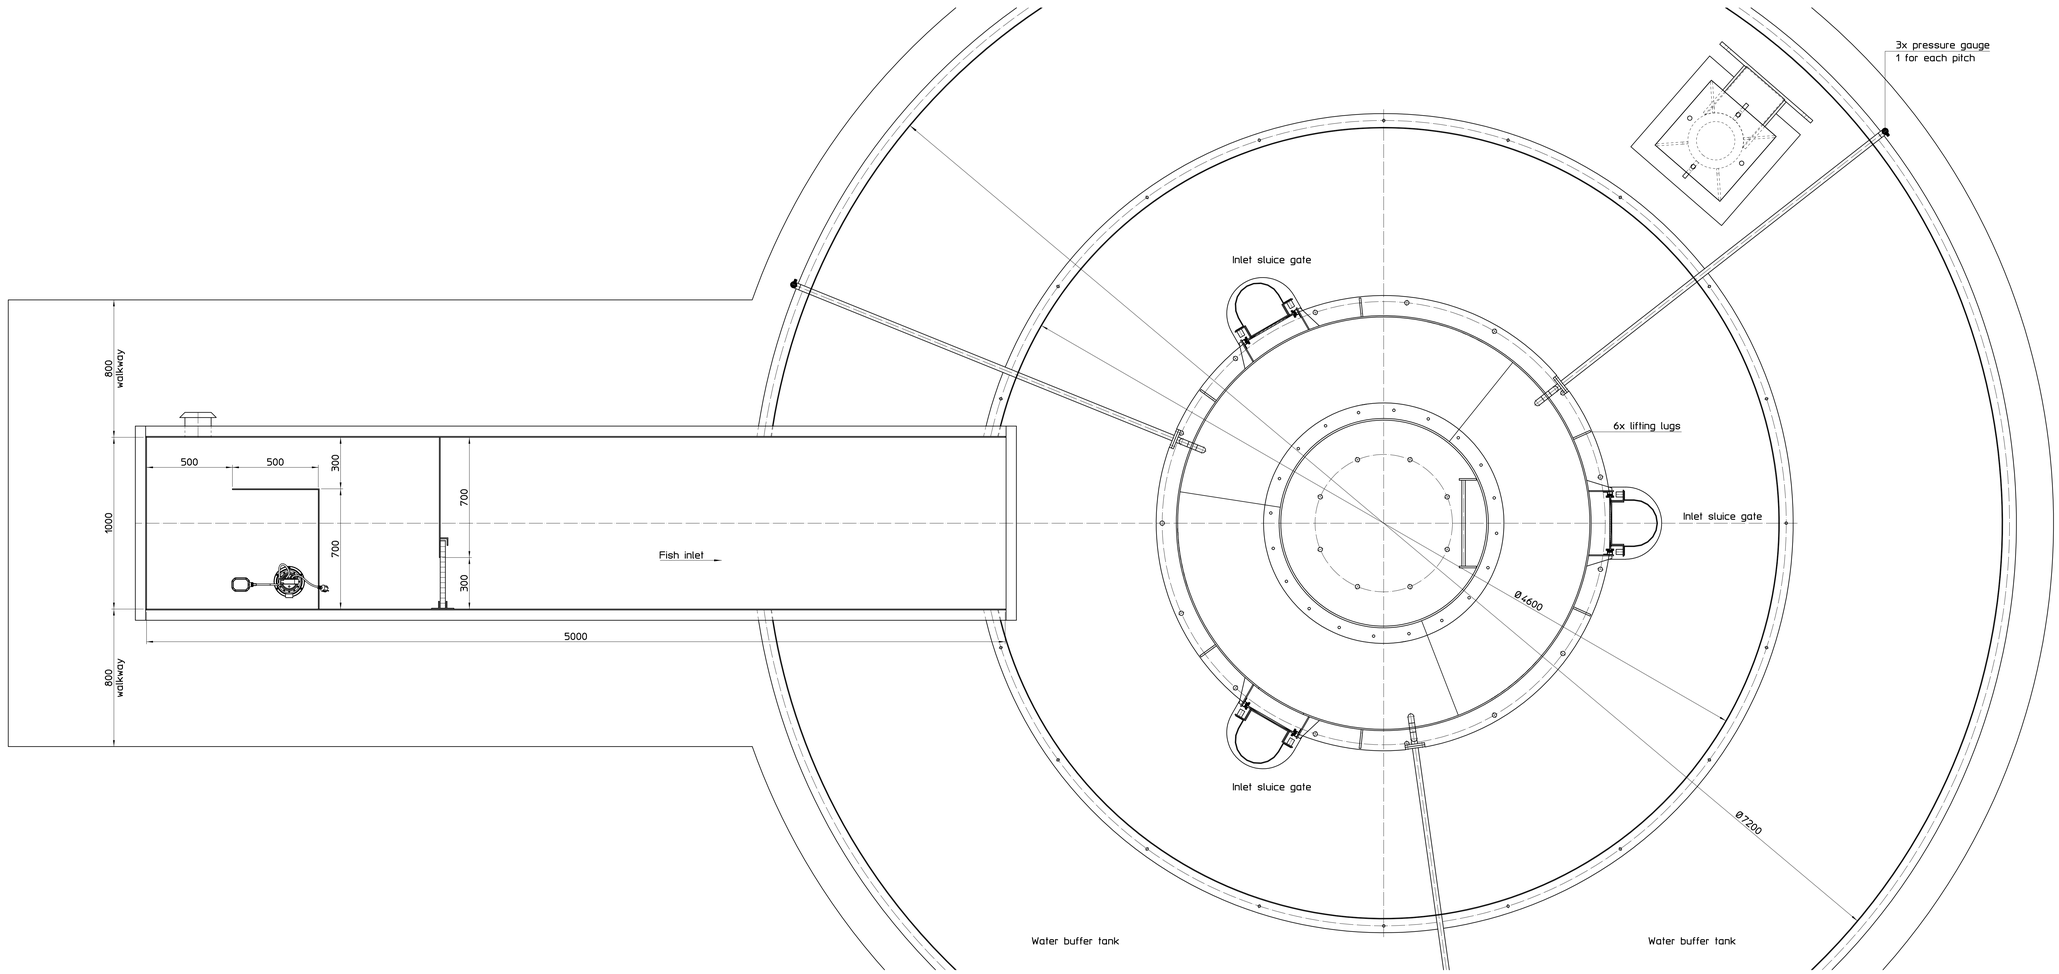

PROPOSED BY

VANDEZANDE

B.V.B.A. VANDEZANDE
Zeepziederijstraat 5
Postbus 62
B-8600 DIKSMUIDE
Tel. 051/50 01 17 ● Fax 051/50 41 17 ● e-mail: info@vandezande.com

PROJECT

Prototype
Fish spiral sluice gate
Test stand - Inlet

Rev	Date	Modifications	Name
-	1-07-22	First edition	D.R.

Drawn by: D.R.	Projektnr: 2022/17
Checked: D.V.	
Scale: 1:12.5	Plannr: V-FISH / 01 / S02 _ Rev
Date: 1/07/2022	

This drawing is property of Vandezande bvba. It may not be reproduced nor handled to others without our written authorization.

filenr 2022/17 / V-FISH / 01 / S01 / _

sys.date 24/05/22