


Fase 1
Upper sluice gate - closed position - no fish
Lower sluice gate - closed position - fish waiting

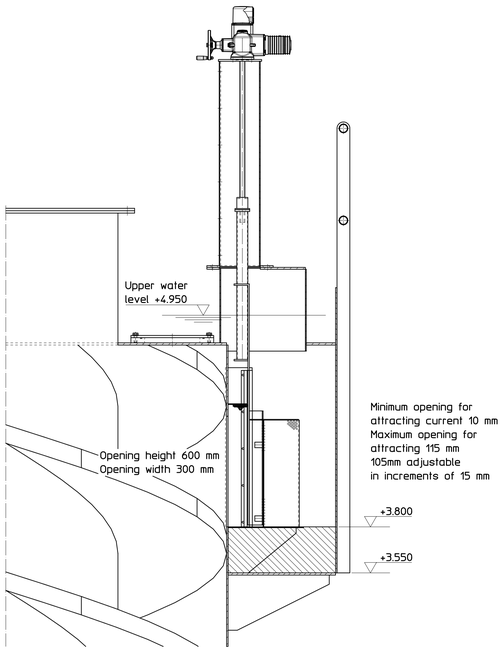


Fase 2
Upper sluice gate - closed position - no fish
Lower sluice gate - open position - fish entry

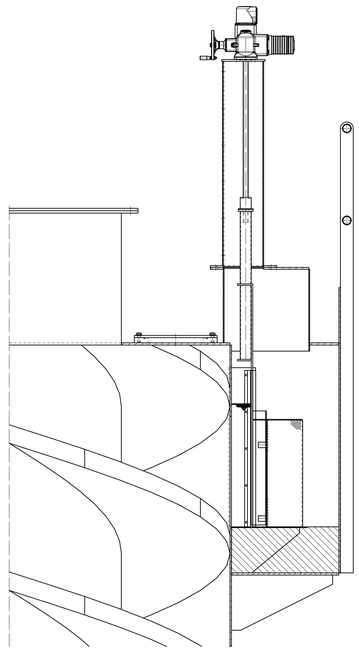

Fase 3
Upper sluice gate - closed position - no fish
Lower sluice gate - closed position - fish migration

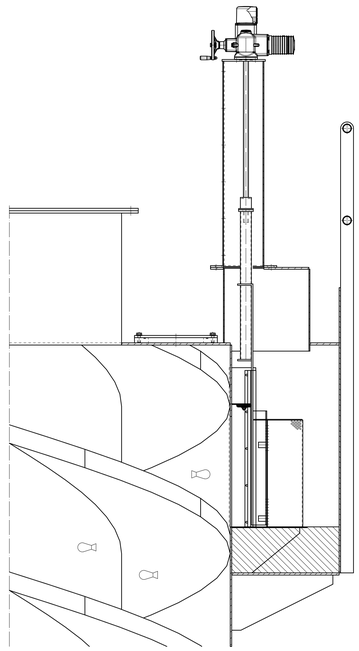



Fase 4
Upper sluice gate - open position - fish outlet
Lower sluice gate - closed position - fish waiting

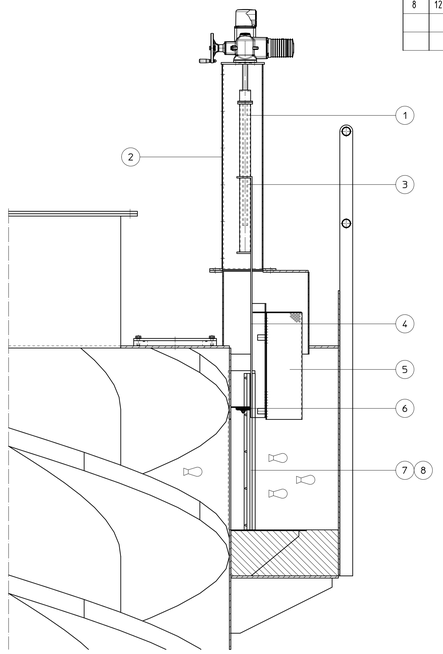



Posnr	Numb	Description	Material
1	6	Spindle nut Tr 28x5	Bronze
2	6	Removable plate for control and maintenance	St 37-2
3	6	Spindle Tr 28x5 - left-hand thread	AISI 316
4	6	Sluice gate - width 315 mm - thickness 8 mm	St 37-2
5	6	Attracting water flow distributor - opening SW 7	St 37-2
6	6	Seal 80x10	NBR
7	12	Sluice gate guidance - type S - model CRU10 - green colour	Plastic
8	12	Mounting profile guidance - type C15V	AISI 316


Section A-A

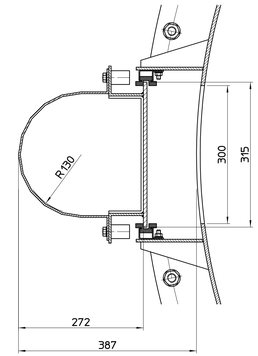

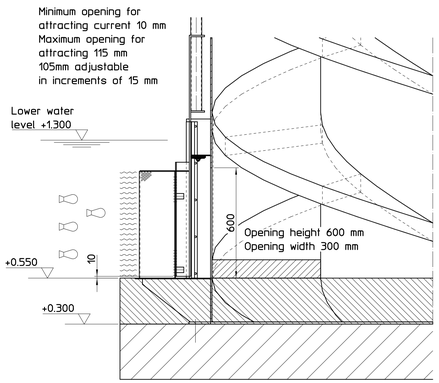

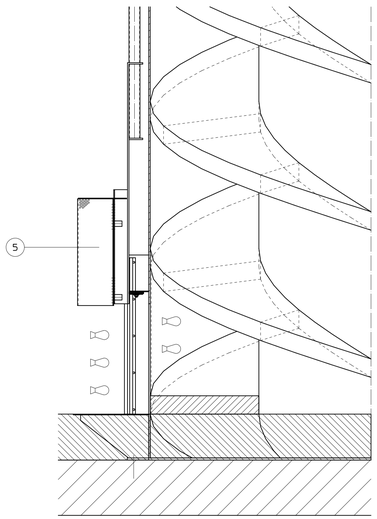

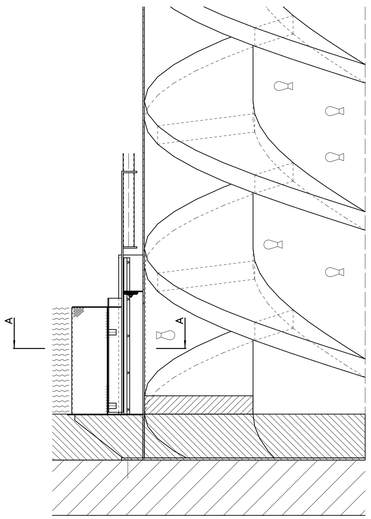

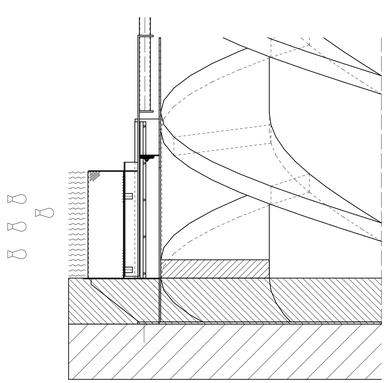

PROPOSED BY

VANDEZANDE
B.V.B.A. VANDEZANDE
Zeepziederijstraat 5
Postbus 62
B-8600 DIKSMUIDE
Tel. 051/50.01.17 • Fax: 051/50.41.17 • e-mail: info@vandezande.com

PROJECT

Prototype
Fish spiral sluice gate
Test stand - Operating principle

Rev.	Date	Modifications	Name
-	1-07-22	First edition	D.R.

Drawn by: D.R.	Projektnr: 2022/17
Checked: D.V.	
Scale: 1:12.5	Plannr: V-FISH / 01 / S04 _ Rev.
Date: 1/07/2022	

This drawing is property of Vandezande bvba. It may not be reproduced nor handled to others without our written authorization.

filenr 2022/17 / V-FISH / 01 / S04 / A

sys.date 21/06/22